
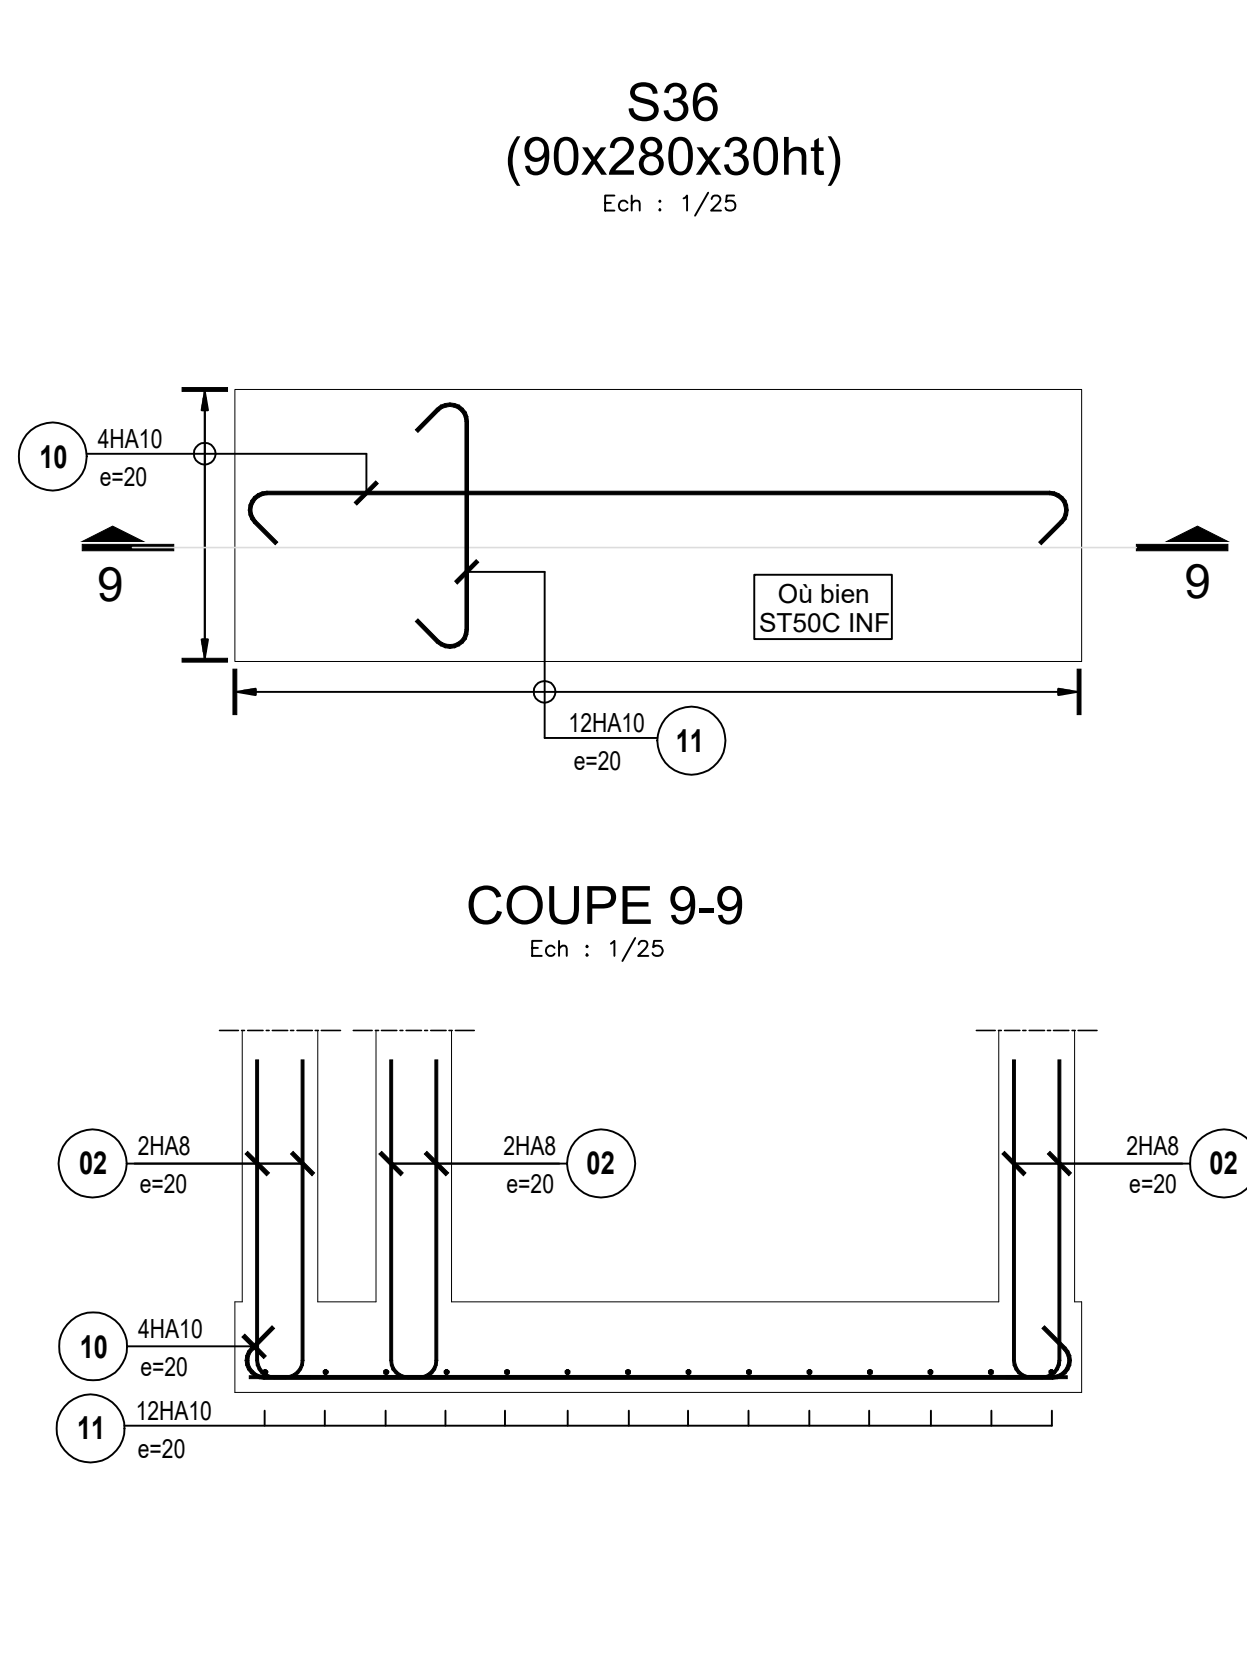
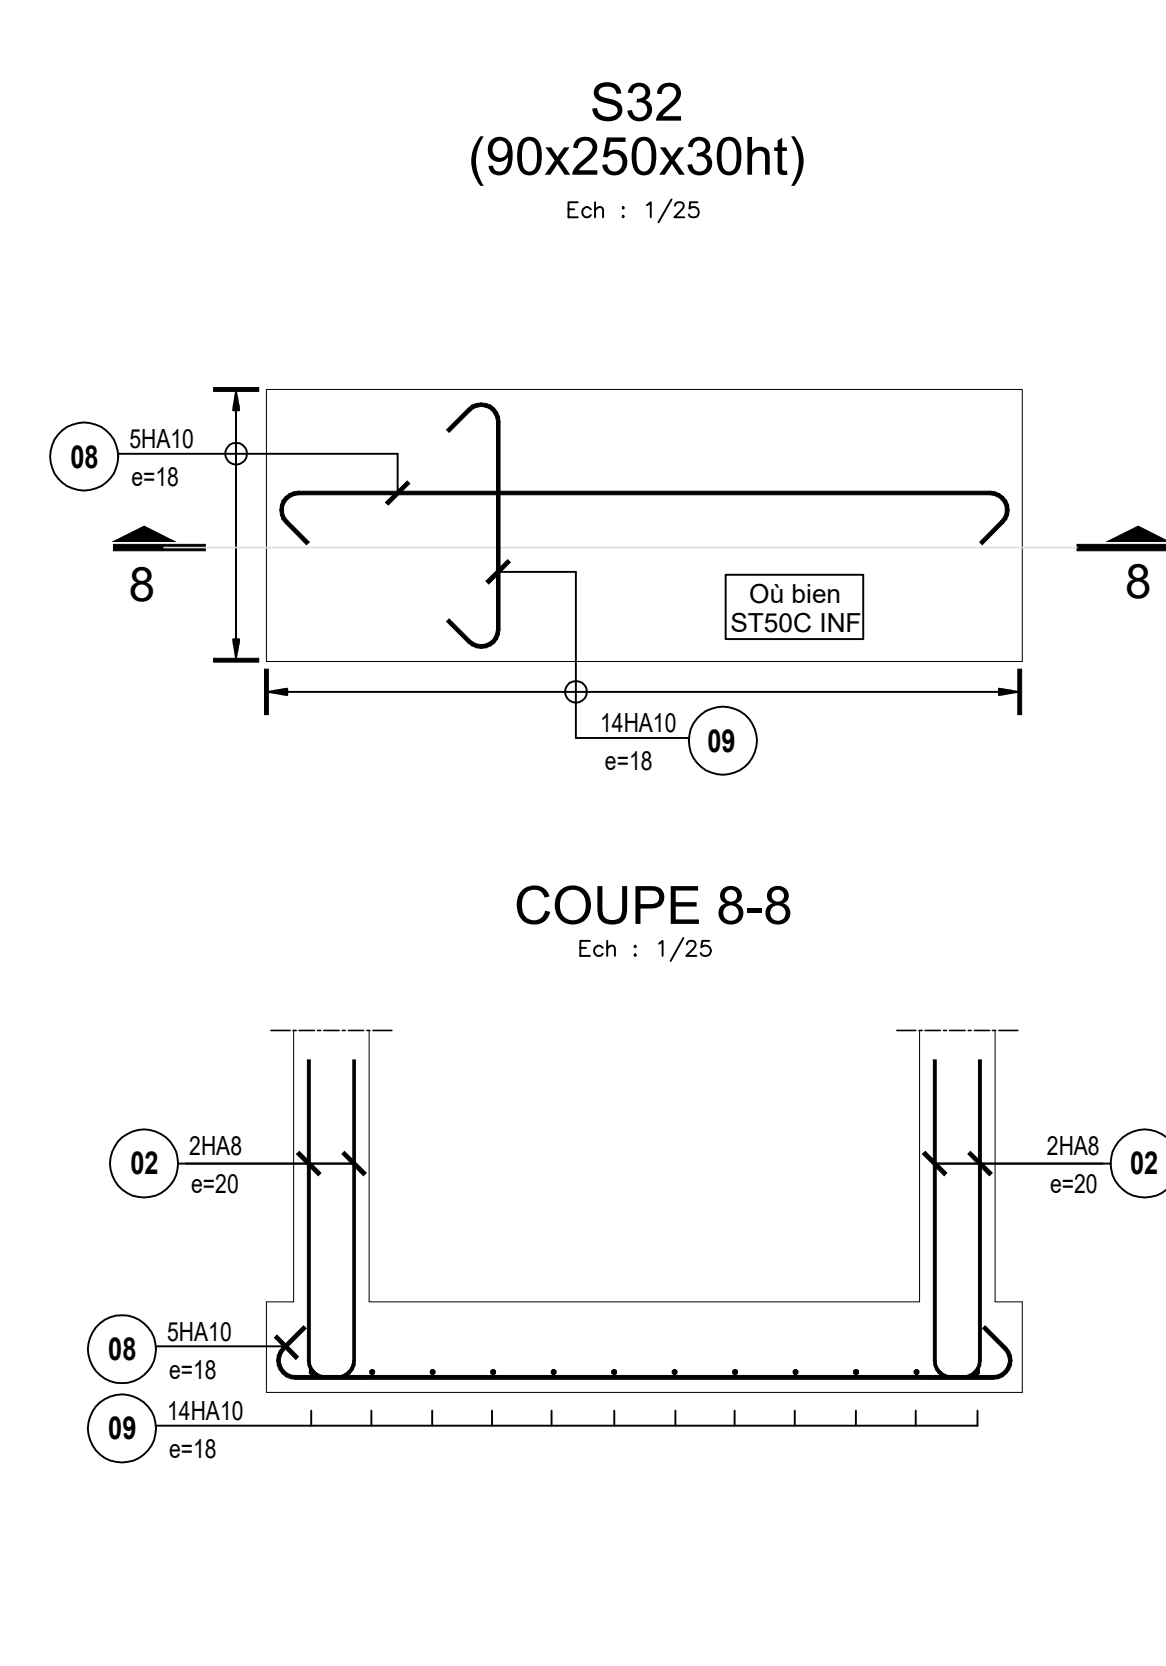
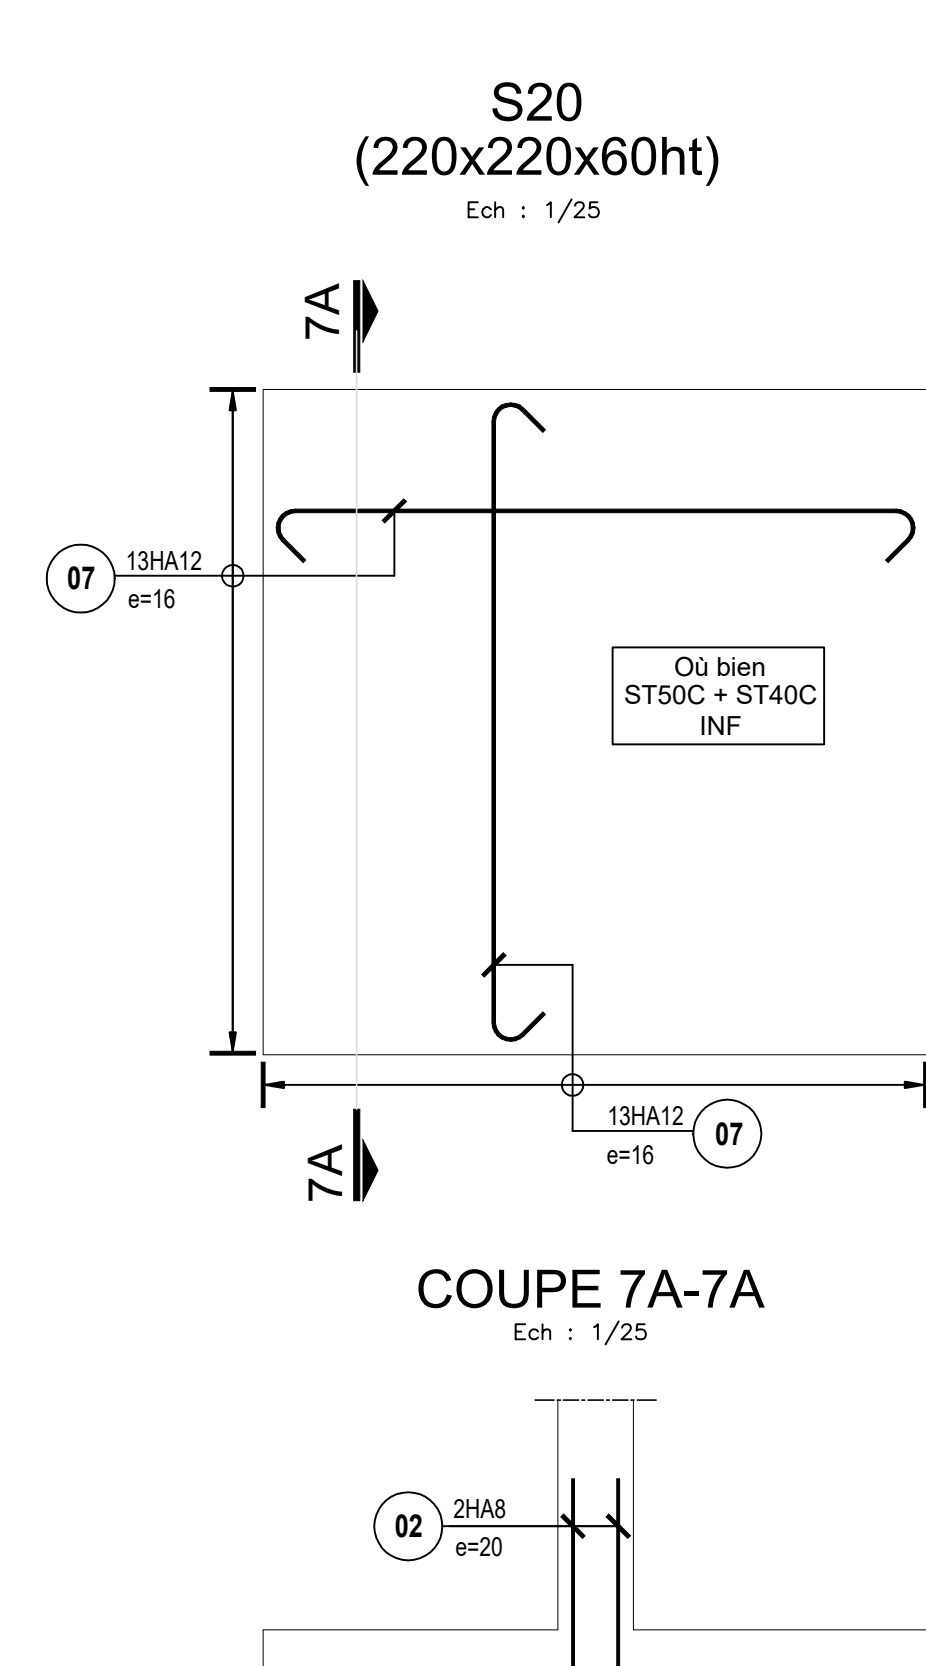
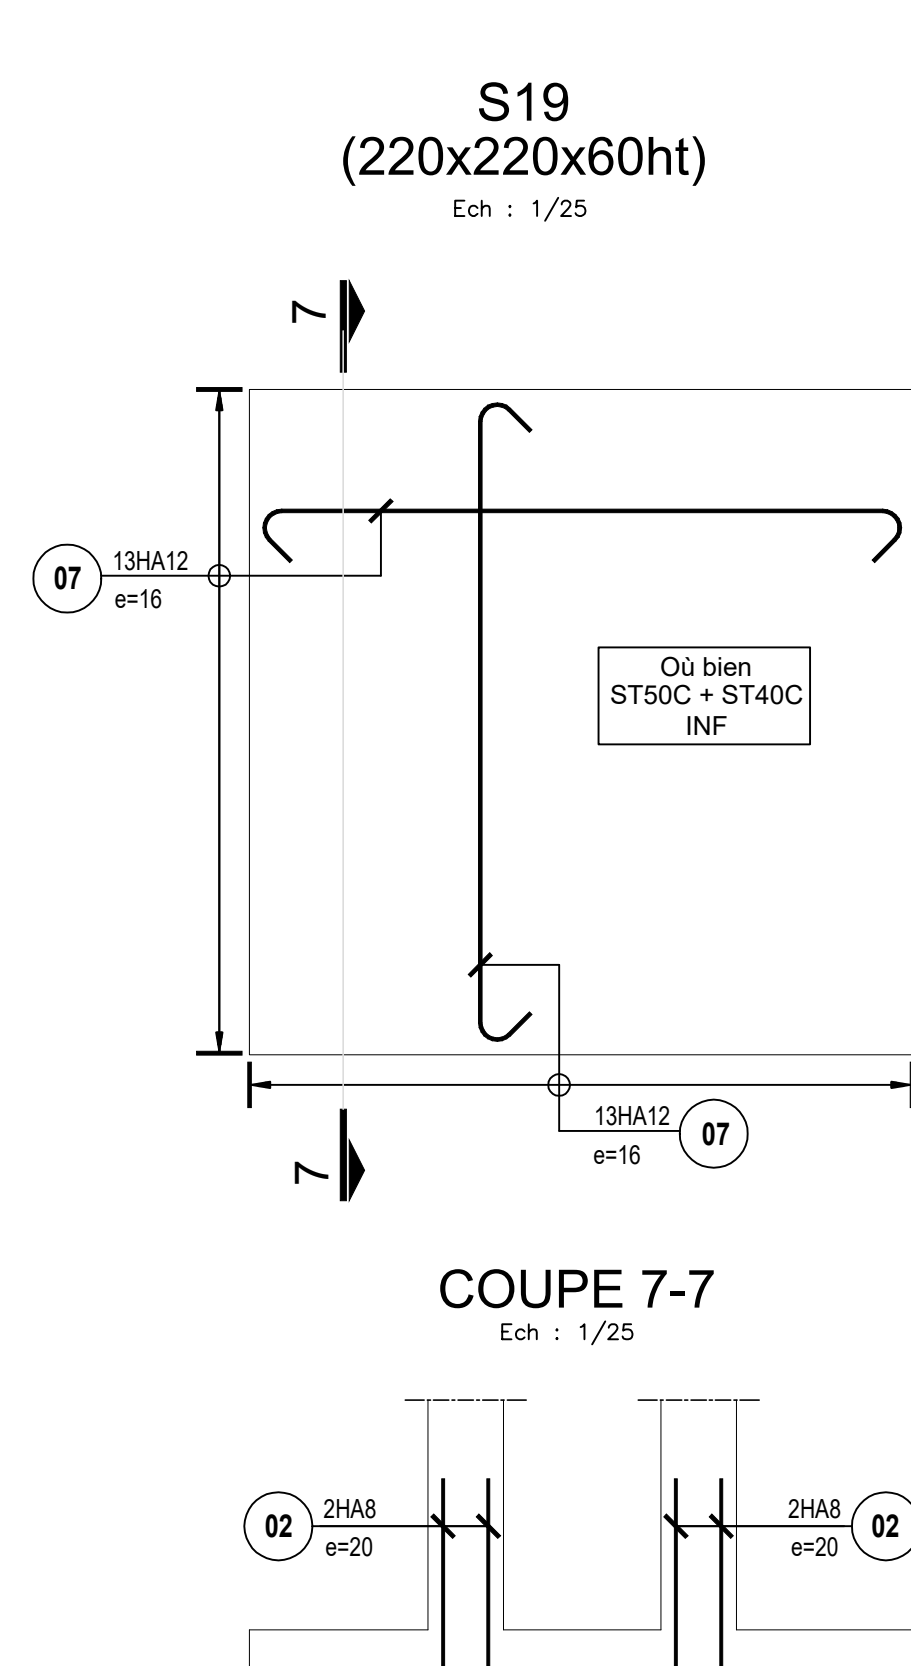
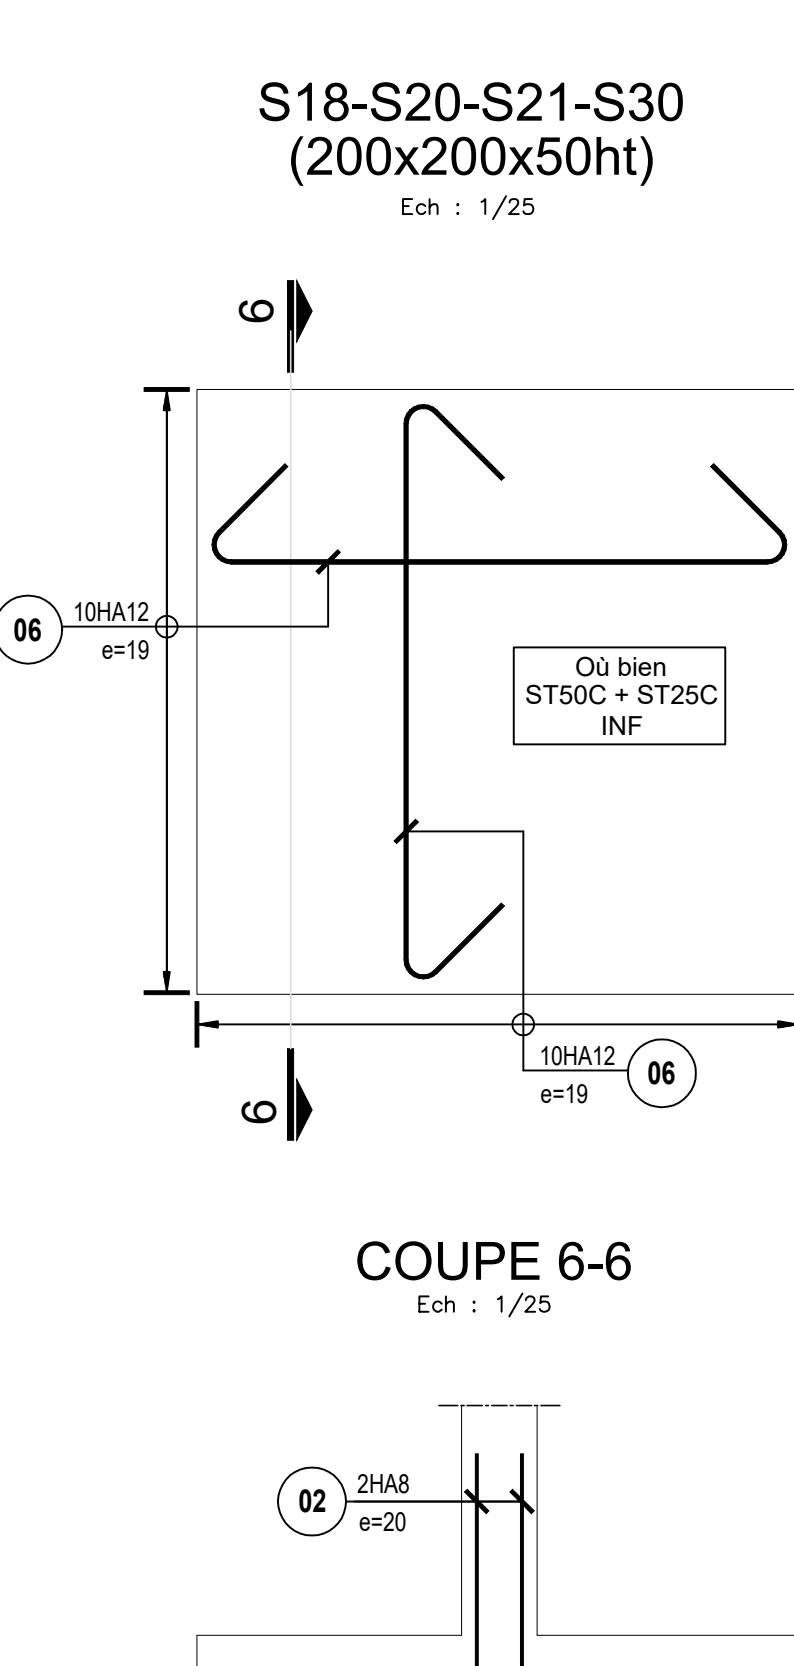
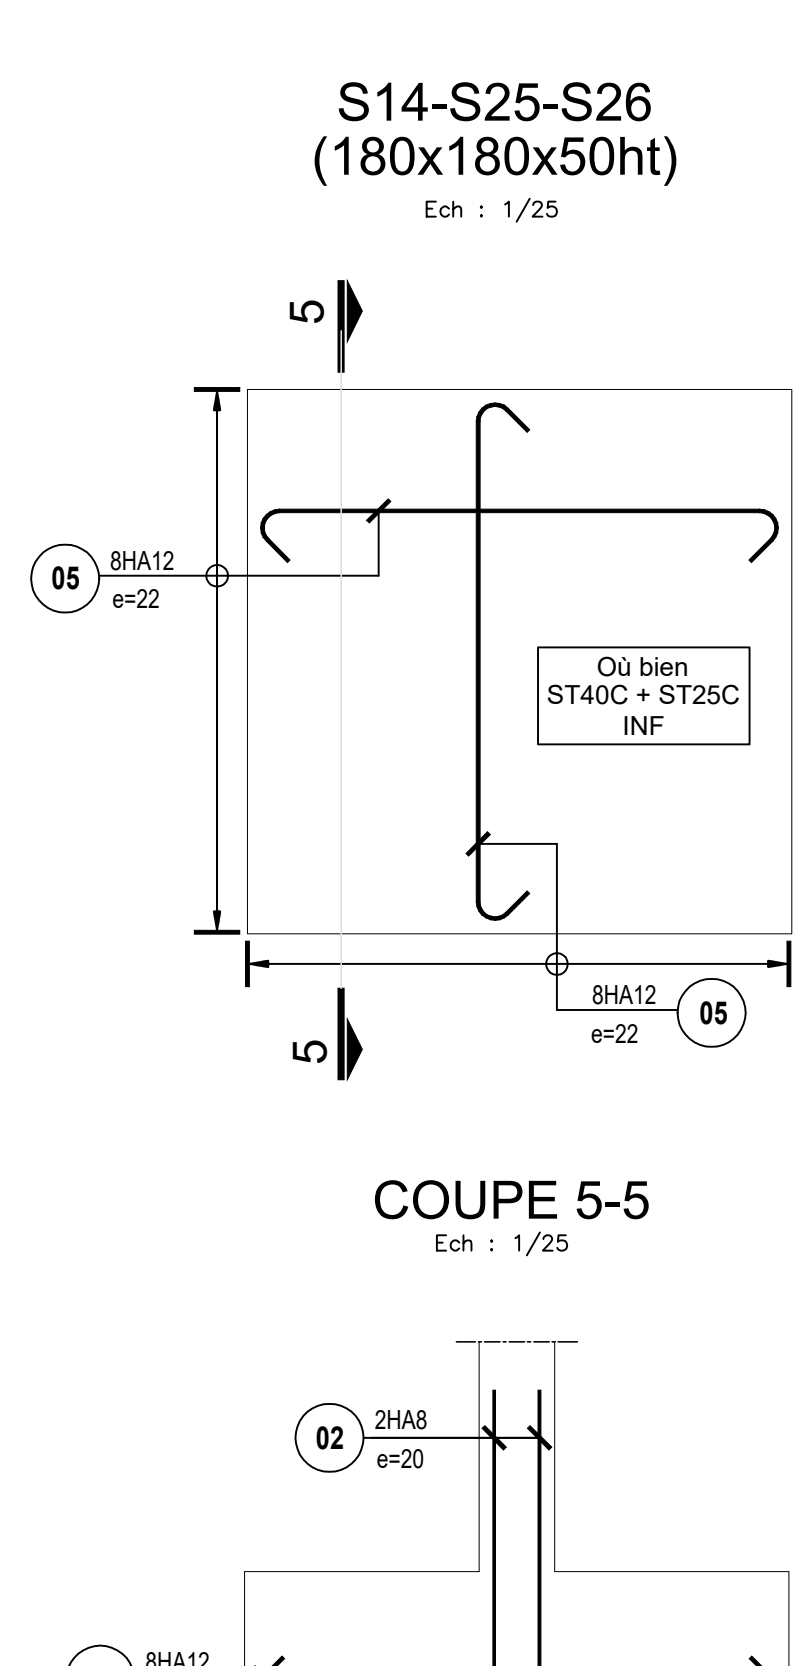
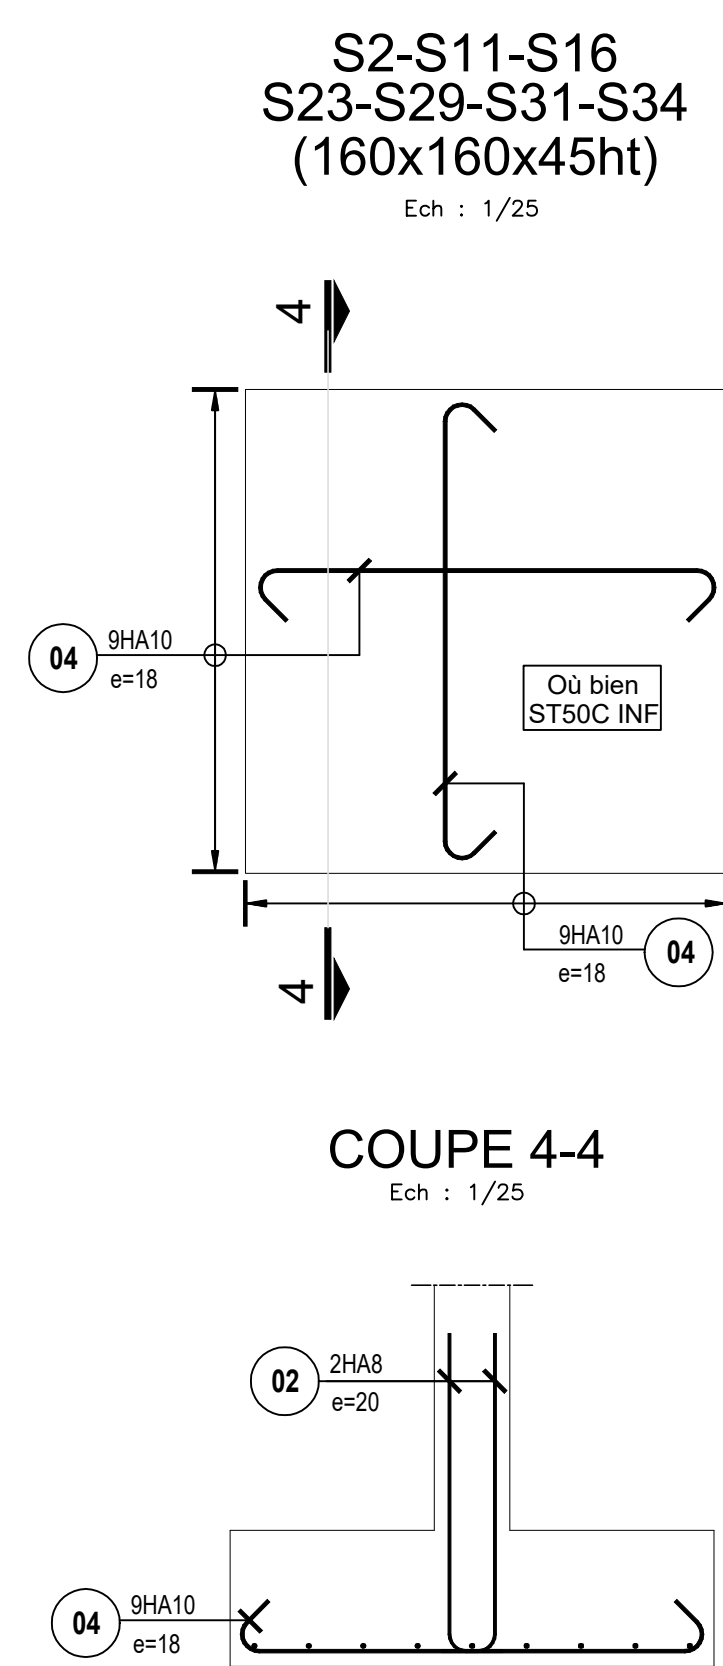
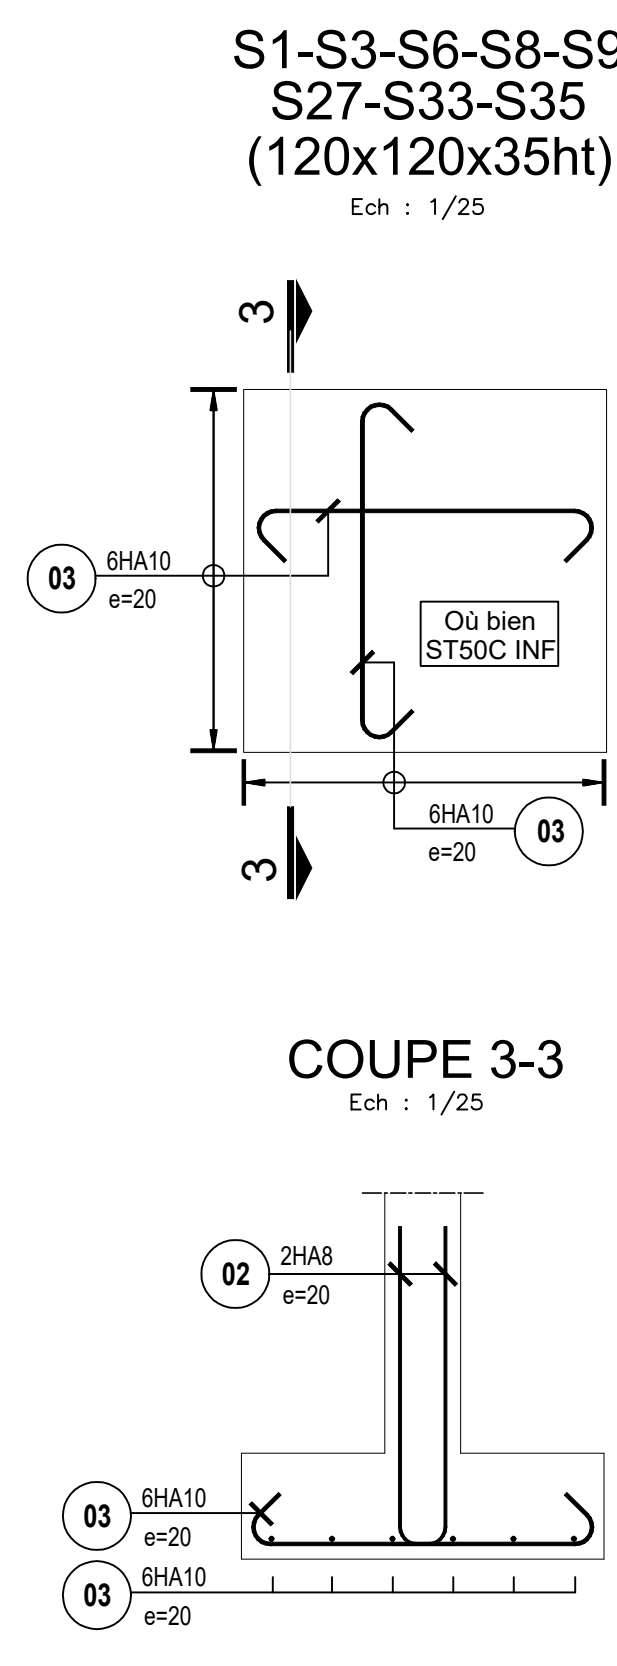
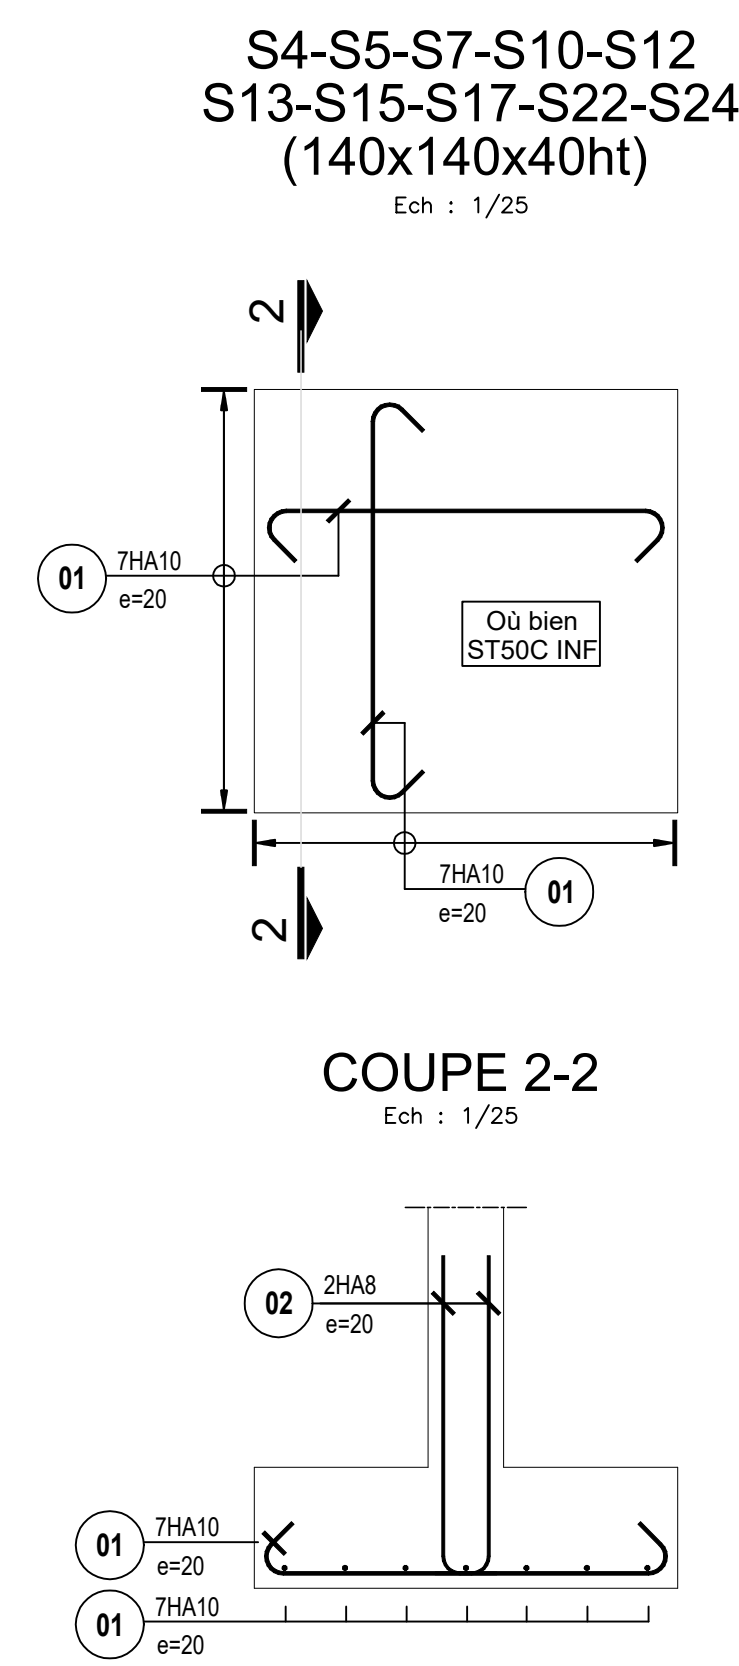
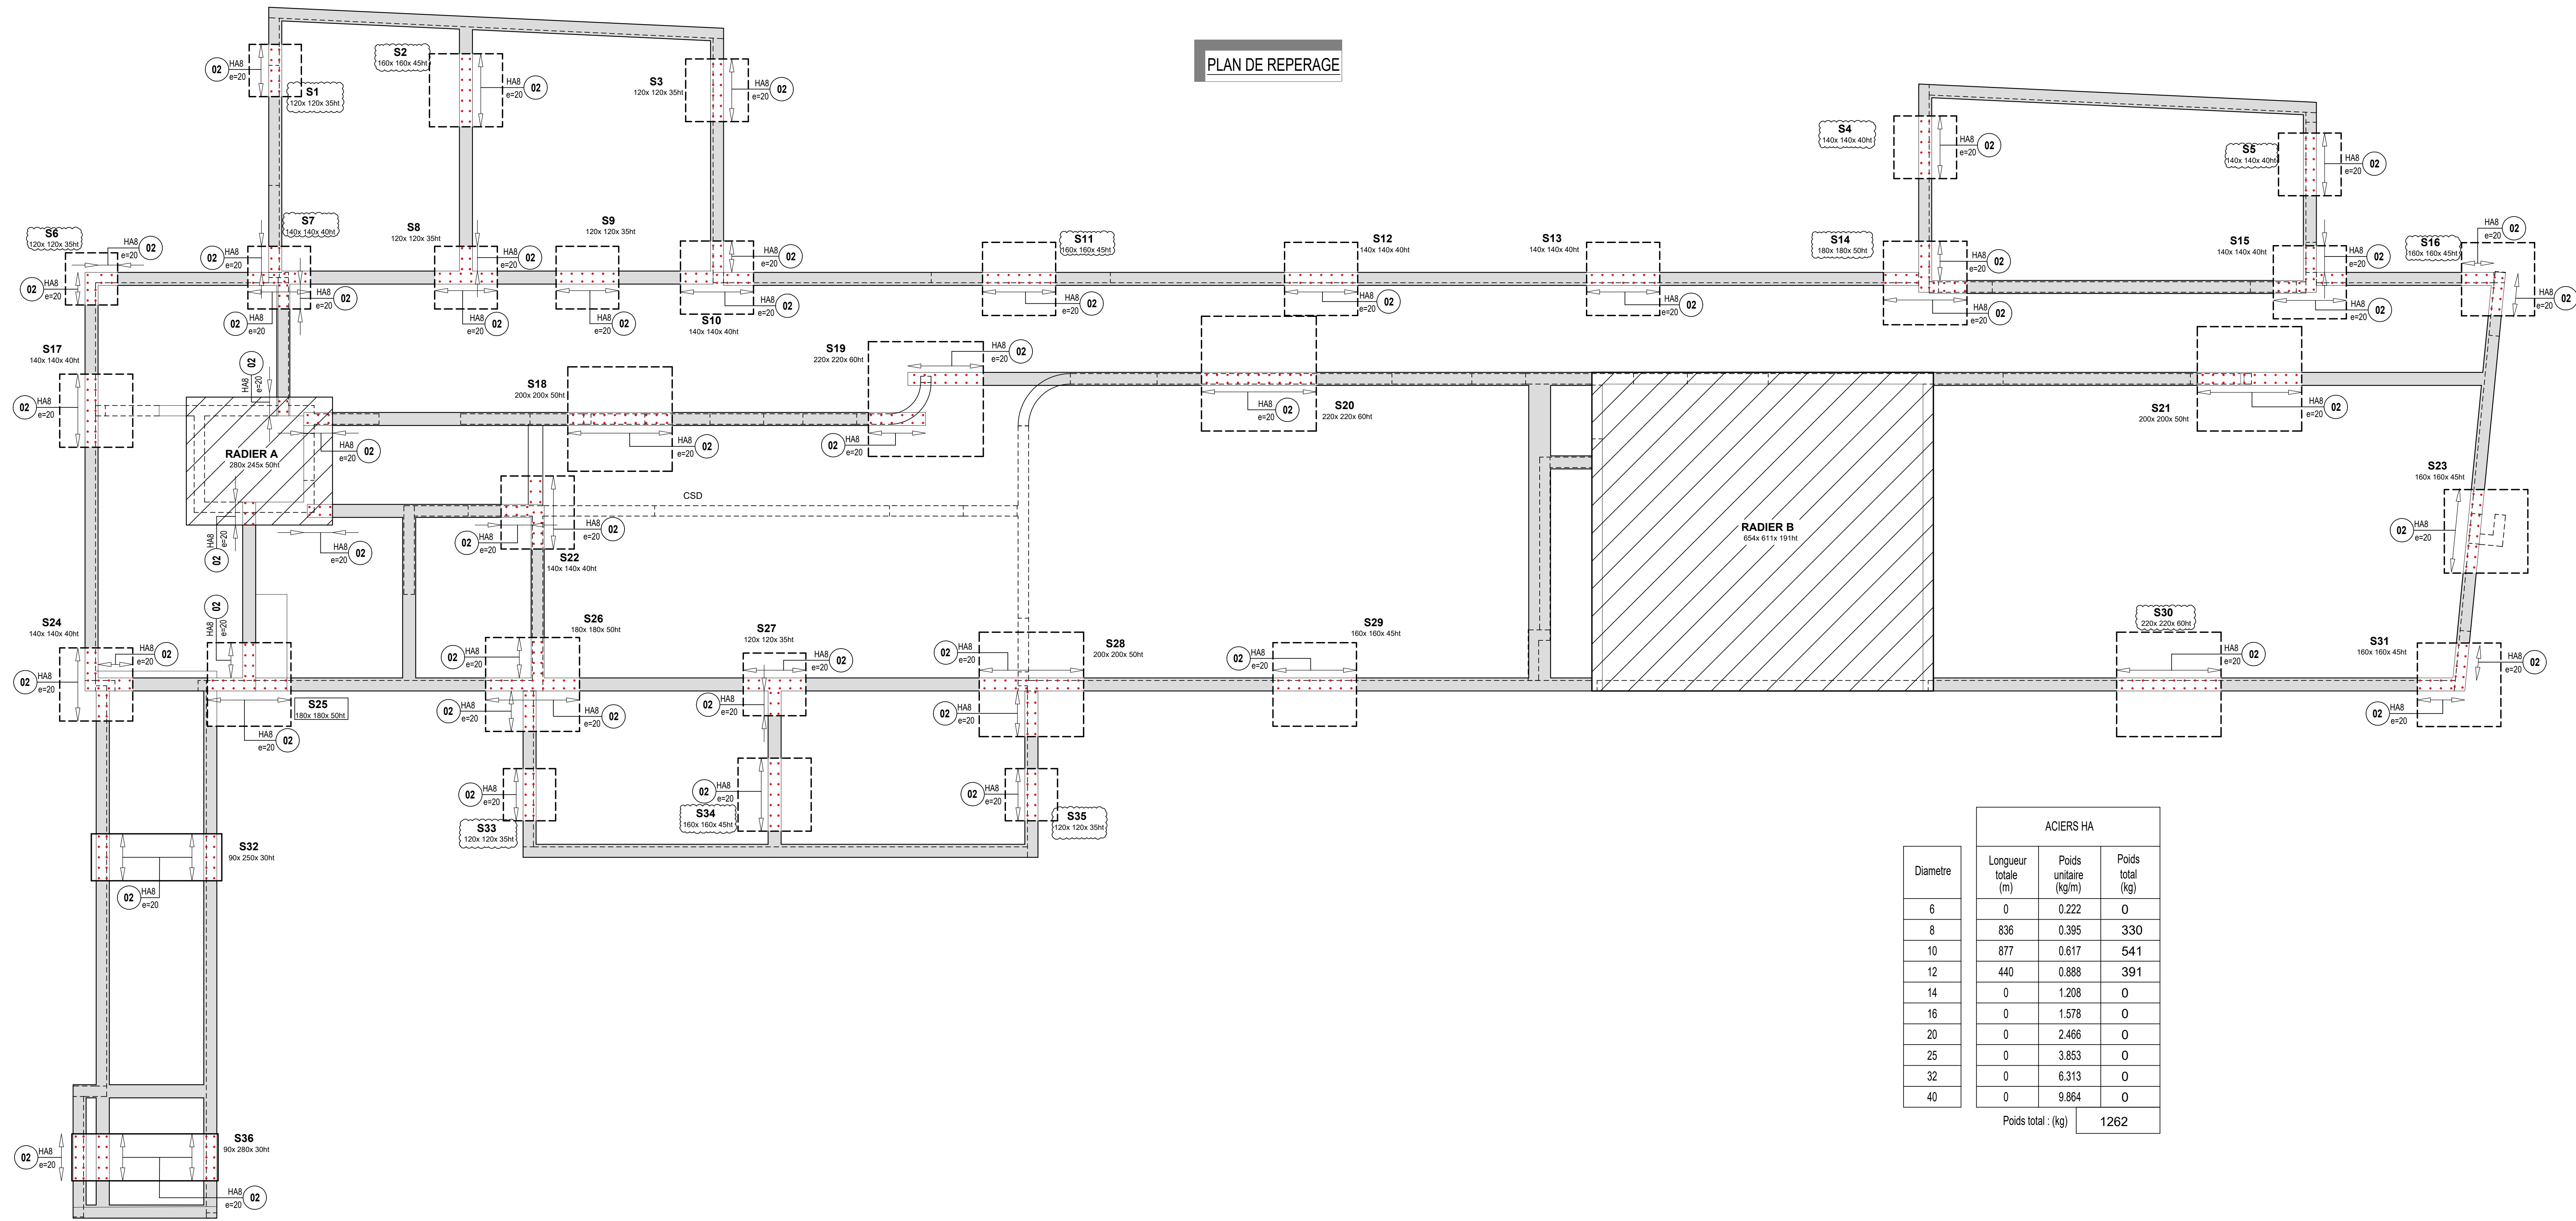


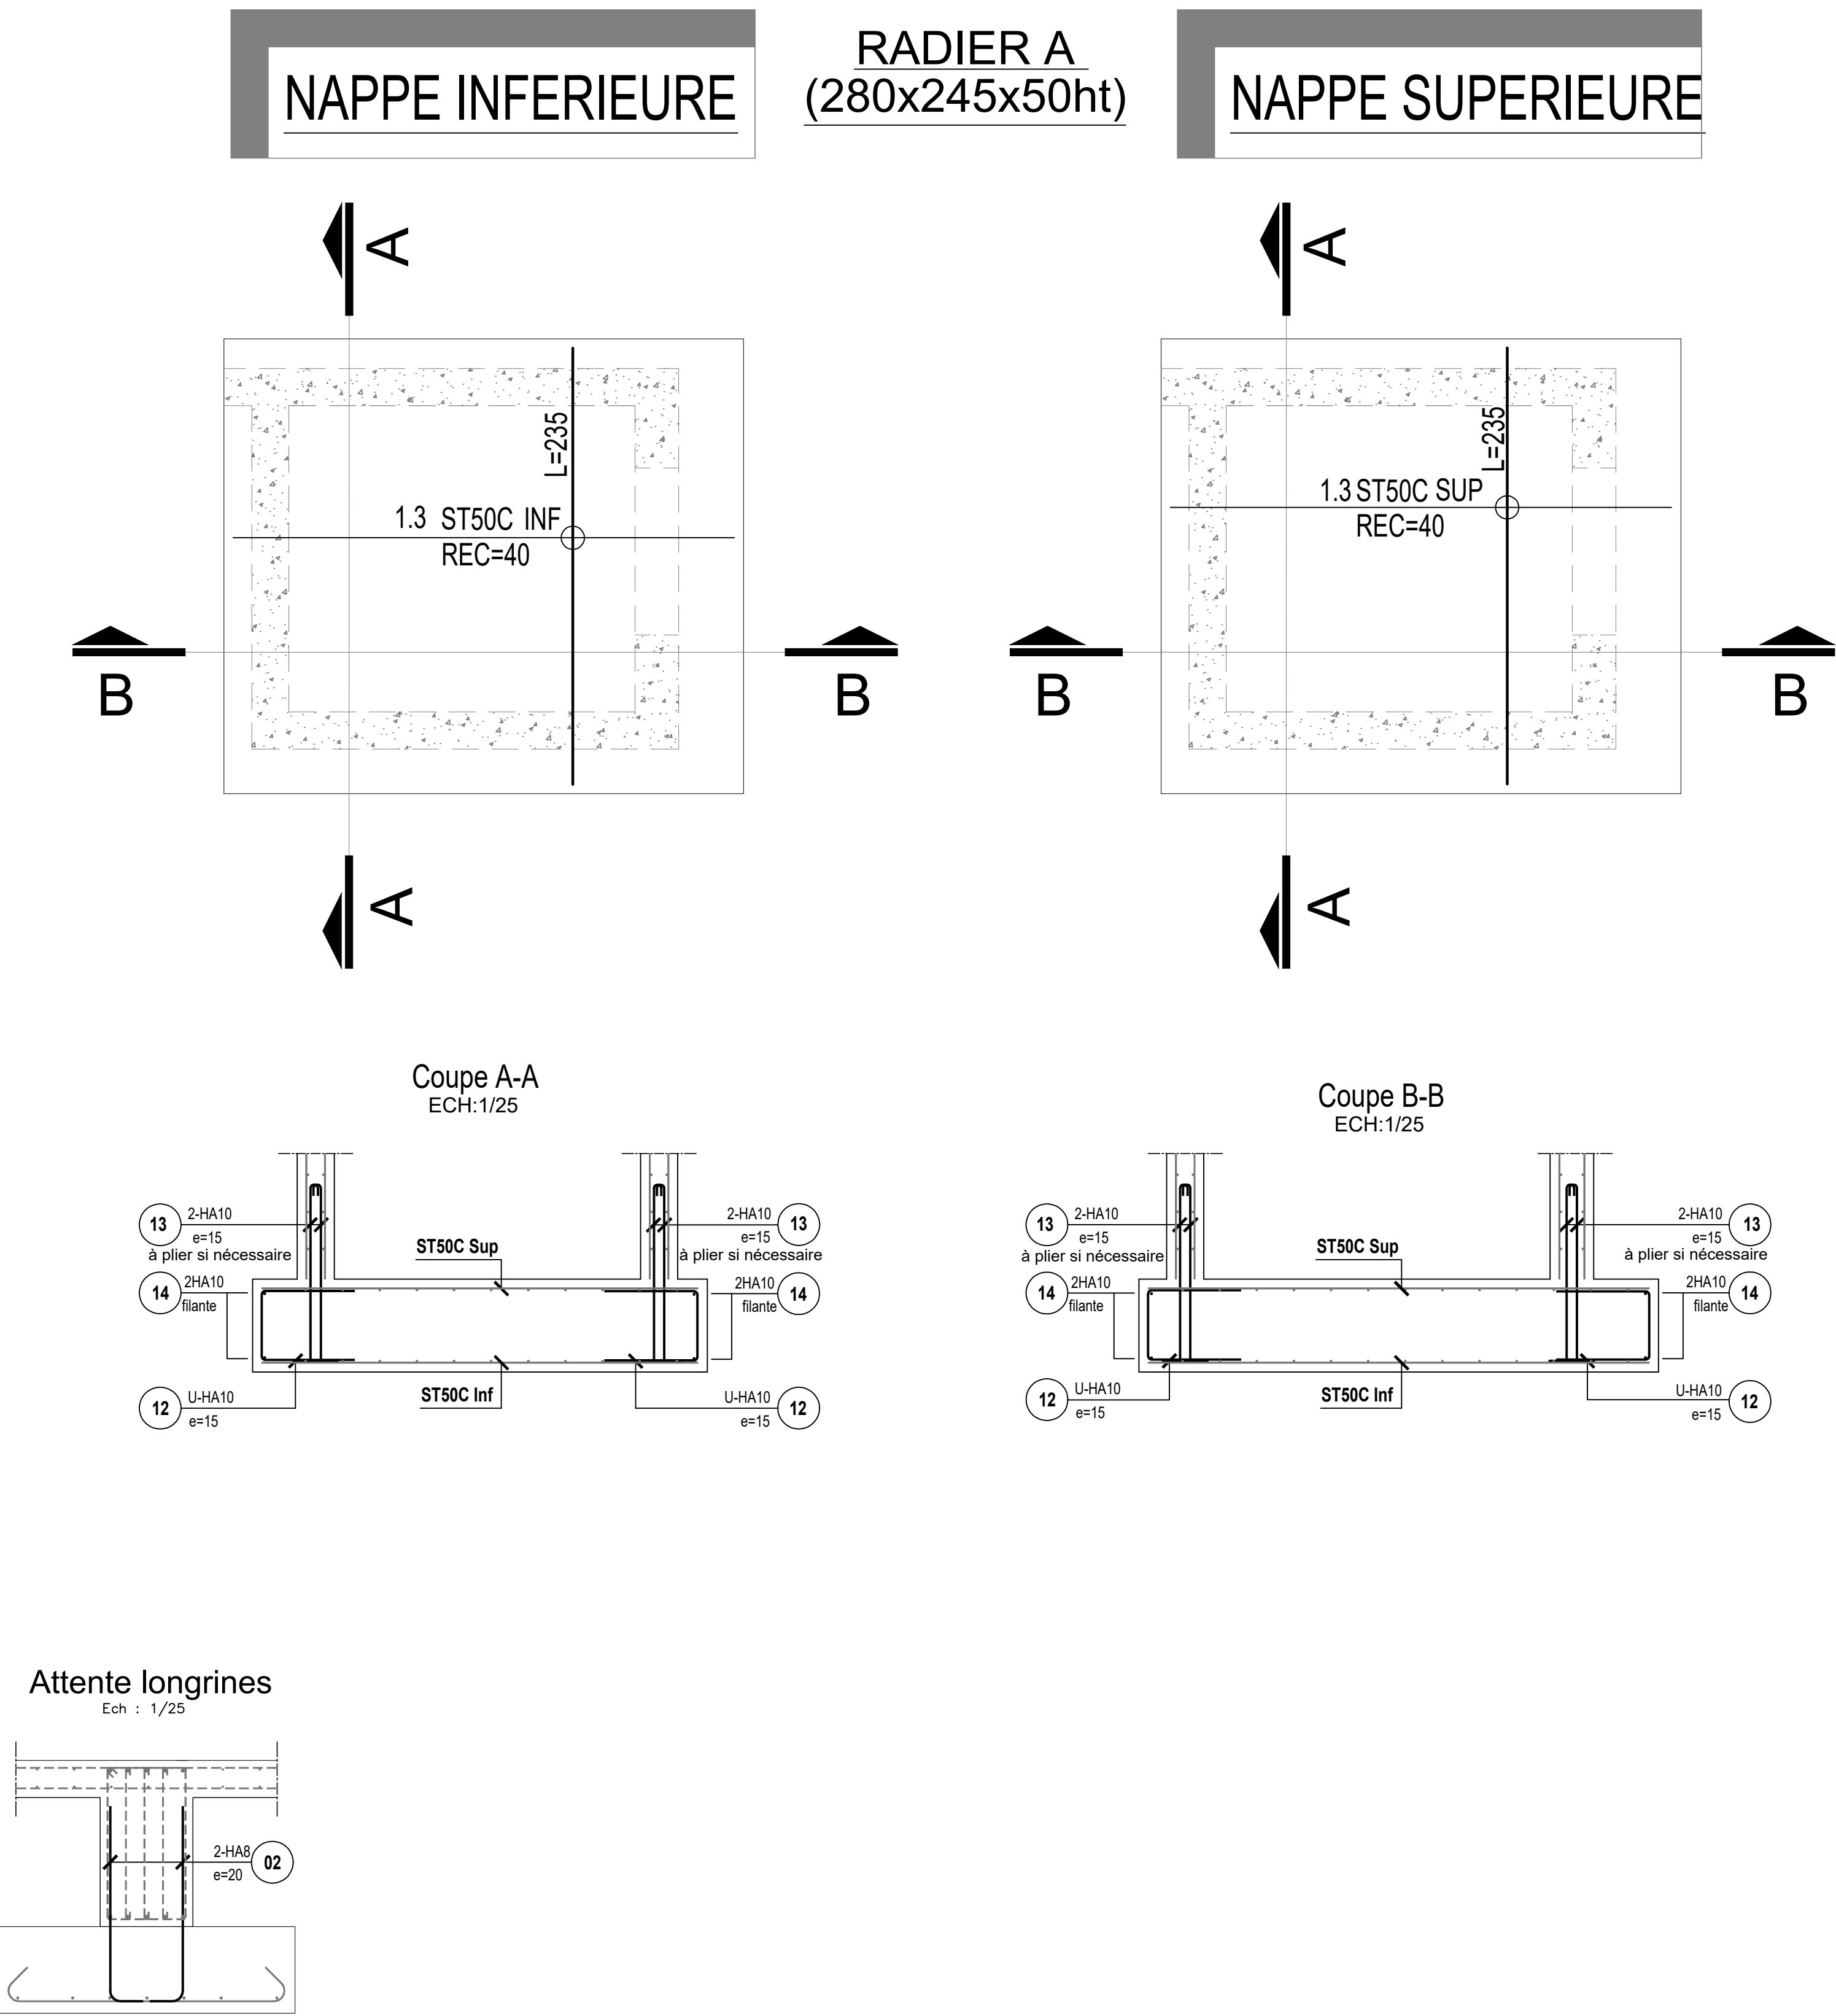

Ce plan ne peut pas servir de coffrage

RESISTANCE DES BETONS
Béton C30/37 (sauf indication contraire)
CLASSE D'EXPOSITION
XAT (sauf indication contraire)
CHARACTERISTIQUE DES ACIERS
S27-S33-S35
S27-S33-S35
S27-S33-S35

PROTECTION DES ACIERS
Pour les aciers de Ø<HA14

Pour les aciers de Ø>HA14

GAGNY

IMMEUBLE DE LOGEMENT ET DE BUREAUX AVEC PARKING EN SOUS-SOL

7 rue danton 92300 LEVALLOIS-PERRET

N°AFFAIRE 04-23

ECHELLE 1/50

F01

INDICE A

FERRAILLAGE SEMELLES & RADIER

VISA MAÎTRE D'OUVRAGE DIRECTION VISA ARCHITECTURE

VISA BUREAU D'ETUDES TECHNIQUES VISA BUREAU DE CONTRÔLE

INDICE DATE OBJET

0 01/03/24

A 03/05/24

Plan réalisé par : C.J.M.H.L.