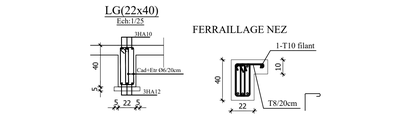

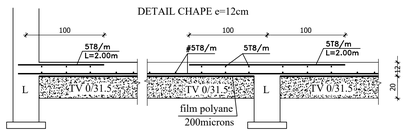

TABLEAU DES SEMELLES

Si	G B	B A	ferraillage	Forme
S1	(130x130xH)	(70x70x25ht)	4T10 e=15	
S2	(160x160xH)	(80x80x30ht)	5T10 e=15	
S3	(180x180xH)	(100x100x30ht)	6T12 e=18	
S4	(220x220xH)	(120x120x30ht)	10T14 e=11	

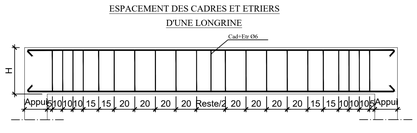

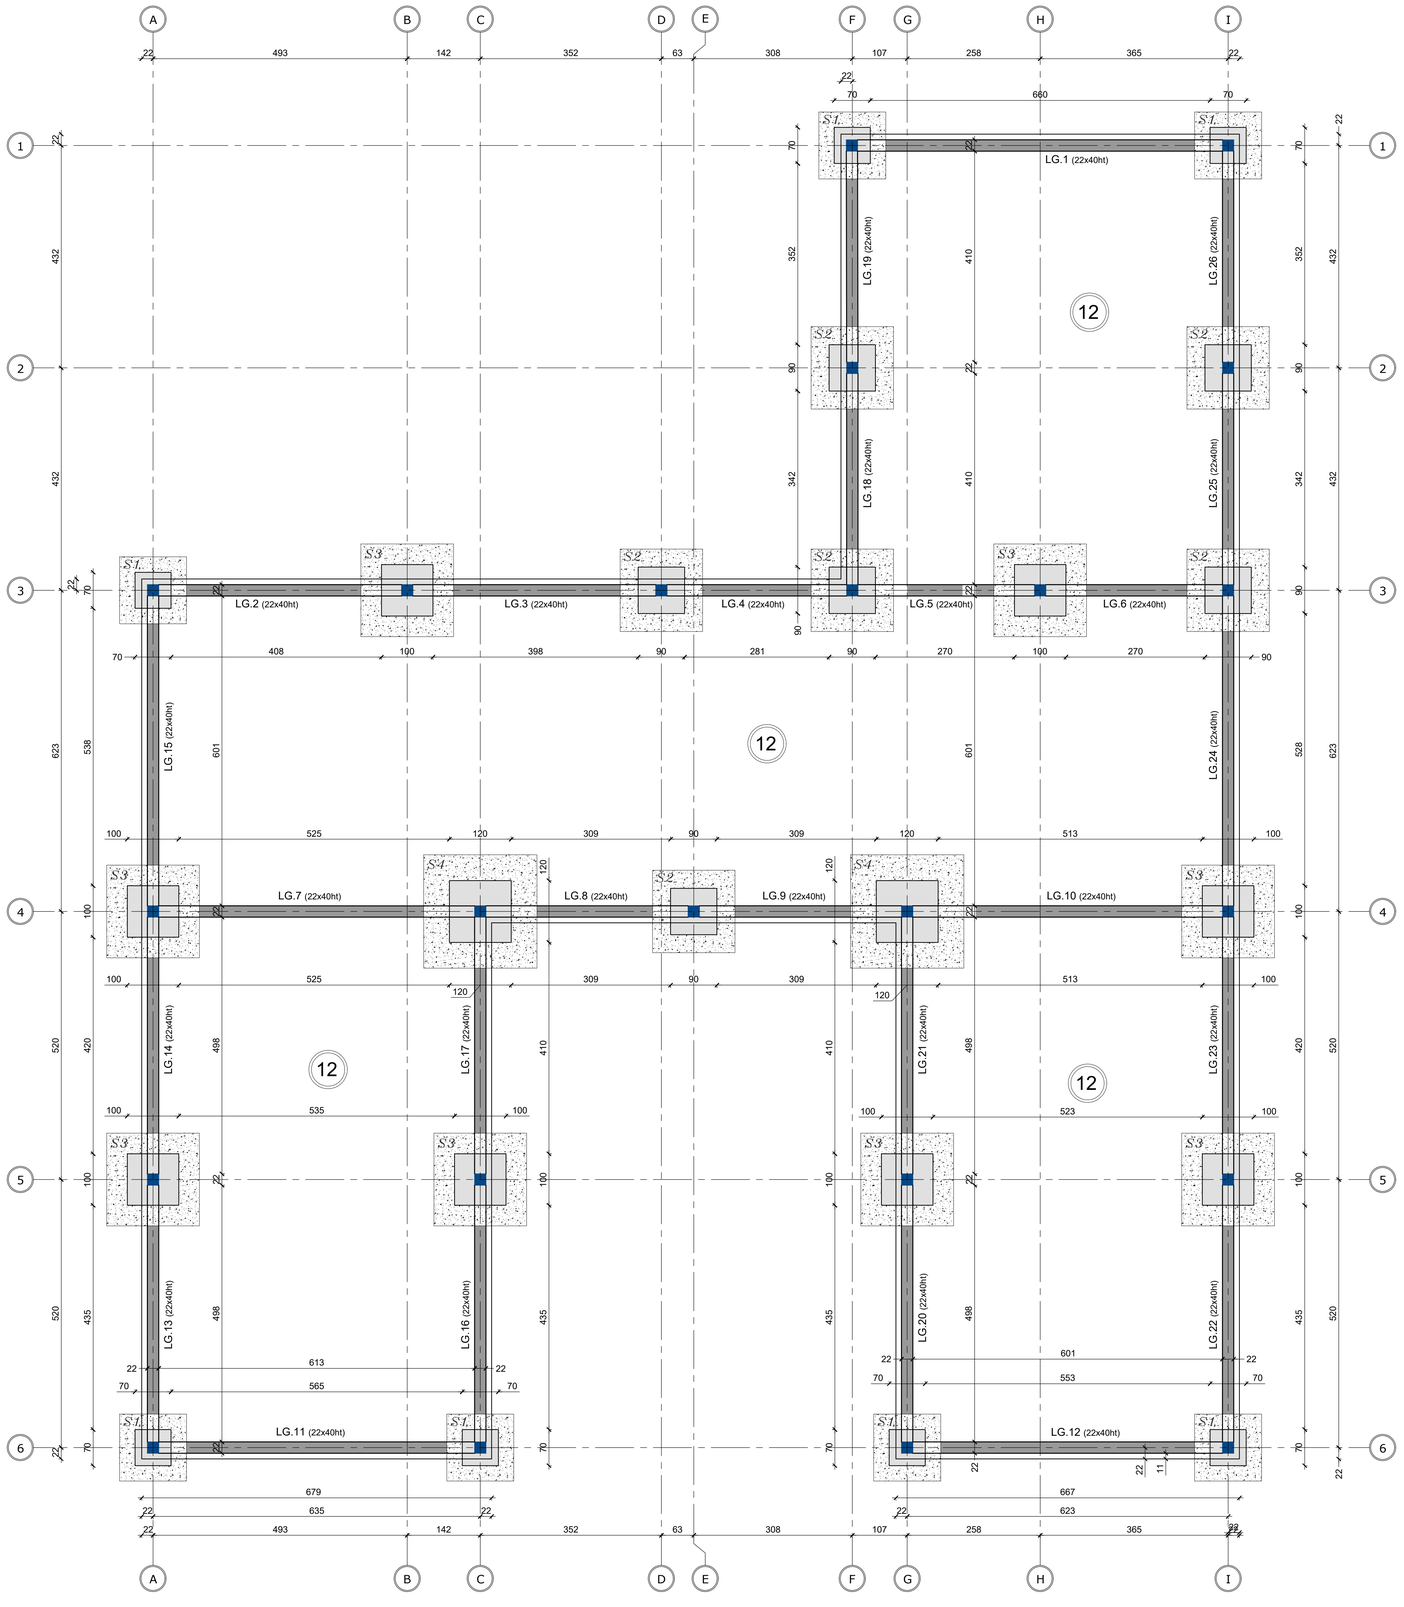

CARACTERISTIQUES DES MATERIAUX

* Béton Arme en fondation:
-Béton en ciment HRS dosé à 400 Kg/m
-Fc 28 = 25 MPa. (Fc28 minimale exigé sur chantier : 25 MPa)
* Nuance d'aciers:
-Acier à haute adhérence Fe=400 MPa.
-Acier doux FE=215 MPa.

NOTA:

* SOL: EN ATTENTE DU RAPPORT GEOTECHNIQUE
-Taux de travail du sol= 1.5bars
-Taux de travail du gros béton= 5bars.
-Niveau d'ancrage sera déterminé lors de l'ouverture du fouille.
* ENROBAGES DES ACIERS:
-5 cm pour les fondations.
-2.5 cm pour la superstructure.

*Pour optimiser le volume du gros béton il faut un rapport Géotechnique

CONSTRUCTION D'UNE VILLA A DJERBA HOUMT SOUK

IND.	DATE	MODIFICATIONS	ETABLI PAR	VERIFIE PAR	APPROUVE PAR
B					
A					
0	03.11.2025	1ère diffusion	H.A	H.A	H.A

PLAN DE COFFRAGE FONDATION

N° DE PLAN: COF 001

INDICE: 0

MAITRE D'OUVRAGE	
ARCHITECTE	
MAITRE D'OEUVRE RENOVATION	
ENTREPRISE GROS OEUVRE	
BET STRUCTURE	
BUREAU DE CONTROLE	

HA CONCEPT
Tél. : +216.23.29.42.29
Mail : engineer.haithem.ayadi@gmail.com

REF. AFFAIRE :	FORMAT :	PHASE :
25040	A1	EXE
DATE 1ère DIFFUSION :	ZONE OU BLOC :	ECHELLE :
03 11 2025	G	1/50 & 1/25