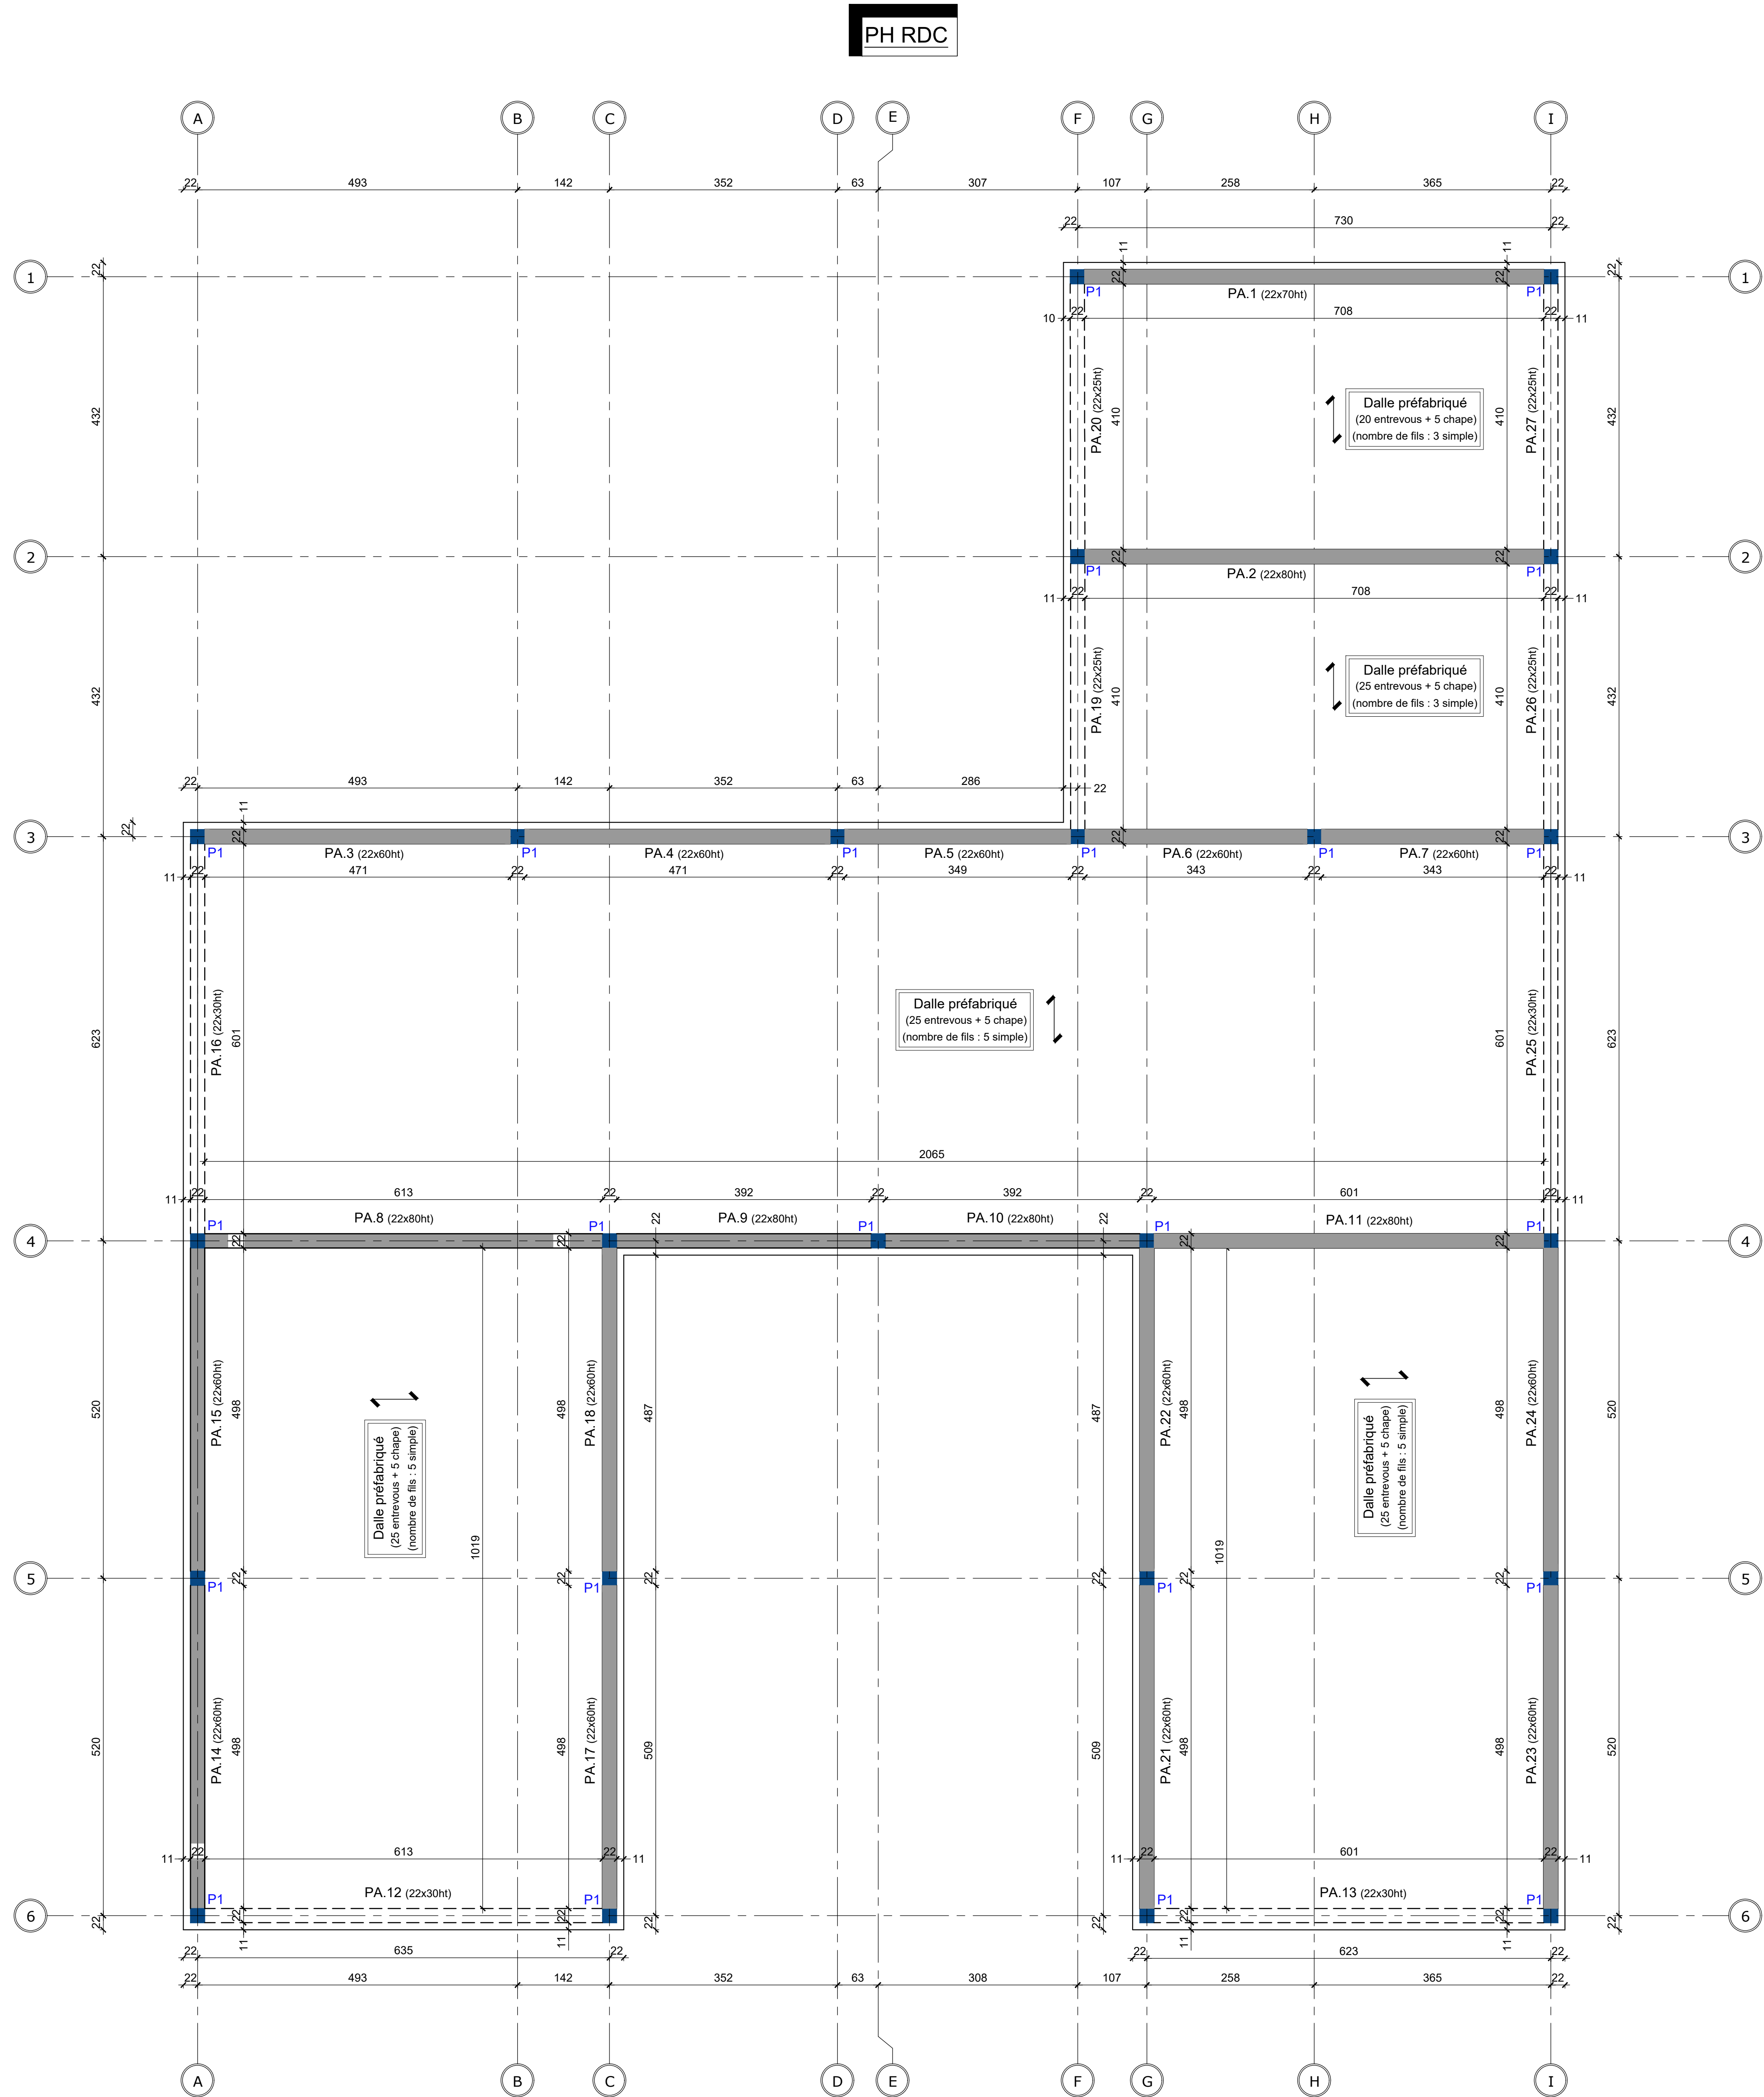


CARACTERISTIQUES DES MATERIAUX

- * Béton Arme en fondation:
- Béton en ciment HRS dosé à 400 Kg/m
 - Fc 28 = 25 MPa. (Fc28 minimale exigé sur chantier : 25 MPa)
- * Nuance d'aciers:
- Acier à haute adhérence Fe=400 MPa.
 - Acier doux FE=215 MPa.

NOTA:

- * SOL: EN ATTENTE DU RAPPORT GEOTECHNIQUE
- Taux de travail du sol= 1.5bars
 - Taux de travail du gros béton= 5bars.
 - Niveau d'ancrage sera déterminé lors de l'ouverture du fouille.
- * ENROBAGES DES ACIERS:
- 5 cm pour les fondations.
 - 2.5 cm pour la superstructure.

*Pour optimiser le volume du gros béton il faut un rapport Géotechnique

CONSTRUCTION D'UNE VILLA A DJERBA
HOUMT SOUK

B					
A					
0	03.11.2025	1ère diffusion	H A	H A	H A
IND.	DATE	MODIFICATIONS	ETABLI PAR	VERIFIE PAR	APPROUVE PAR

PLAN DE COFFRAGE PH RDC

N° DE PLAN

COF 002

0

INDICE

MAITRE D'OUVRAGE	
ARCHITECTE	
MAITRE D'OEUVRE RENOVATION	
ENTREPRISE GROS OEUVRE	
BET STRUCTURE	
BUREAU DE CONTROLE	



HA CONCEPT

Tél. : +216.23.29.42.29
Mail : engineer.haithem.ayadi@gmail.com

REF. AFFAIRE :	FORMAT :	PHASE :
25040	A1	EXE
DATE 1ère DIFFUSION :	ZONE OU BLOC :	ECHELLE :
03 11 2025	G	1/50 & 1/25